FRONT ELEVATION

SCALE – 8 FEET TO AN INCH

SIDE ELEVATION

SCALE – 8 FEET TO AN INCH

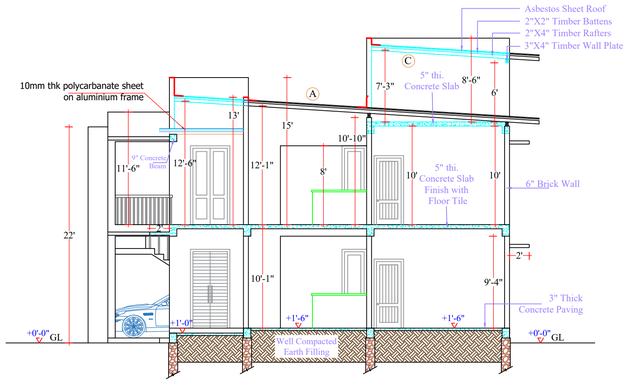

SECTION A-A

SCALE – 8 FEET TO AN INCH

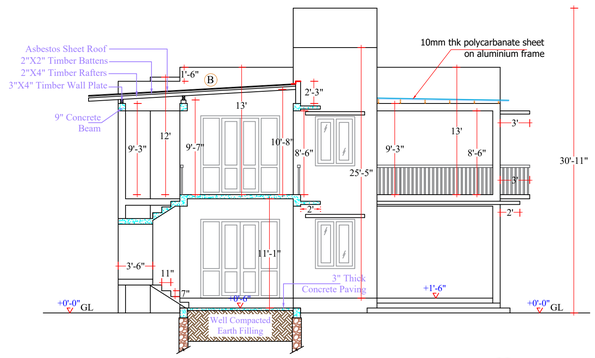

SECTION B-B

SCALE – 8 FEET TO AN INCH

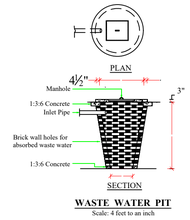

WASTE WATER PIT

Scale: 4 feet to an inch

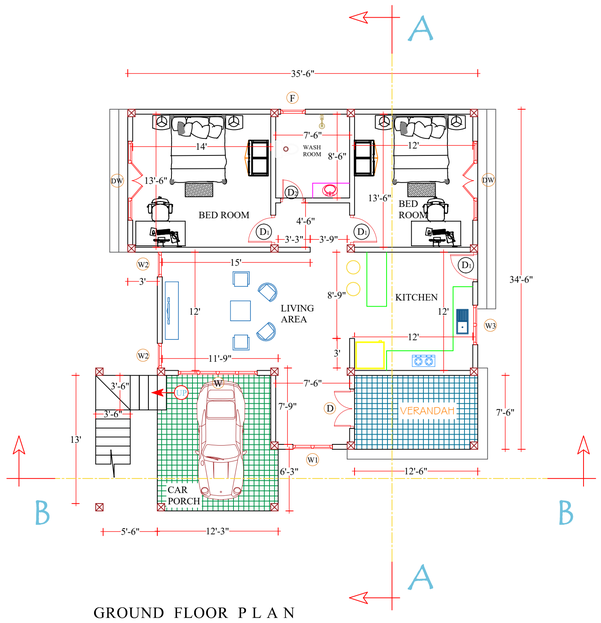

GROUND FLOOR PLAN

SCALE – 8 FEET TO AN INCH

GROUND FLOOR AREA - 1241 square ft

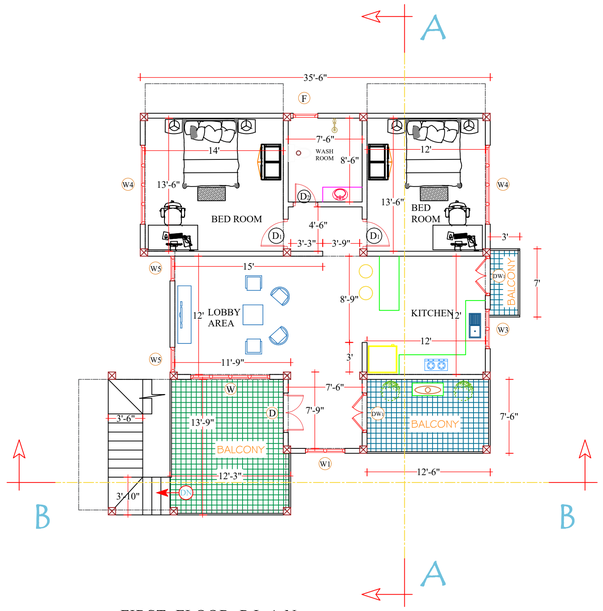

FIRST FLOOR PLAN

SCALE – 8 FEET TO AN INCH

GROUND FLOOR AREA - 1262 square ft

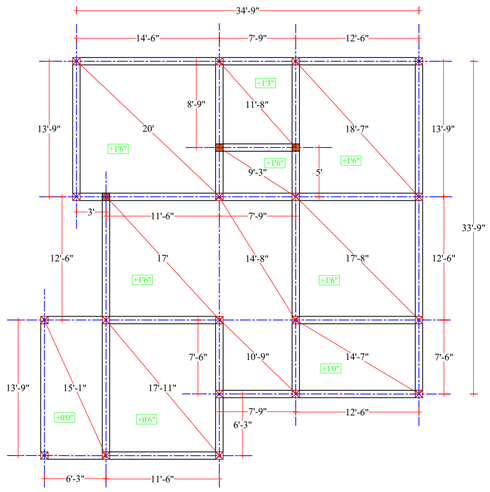

SETTING OUT PLAN

SCALE – 8 FEET TO AN INCH

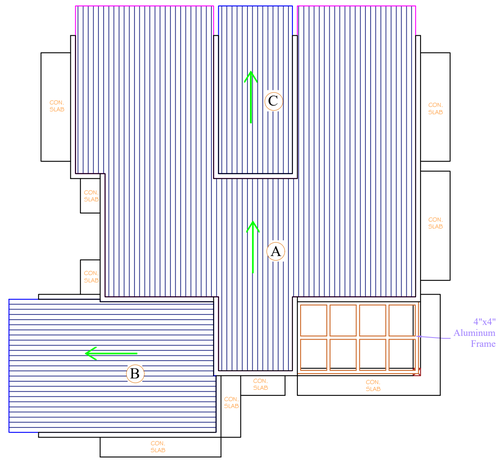

ROOF PLAN

SCALE – 8 FEET TO AN INCH

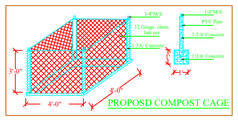

ENGINEER SIGNATURE

DESIGN BY

APPLICANT SIGNATURE

SCALE :- AS GIVEN

DRAWING NUMBER :-DA/25/15

DATE :- 2025/03/30

GROUND FLOOR AREA	- 1241 square ft
FIRST FLOOR AREA	- 1262 square ft
TOTAL FLOOR AREA	- 2503 square ft

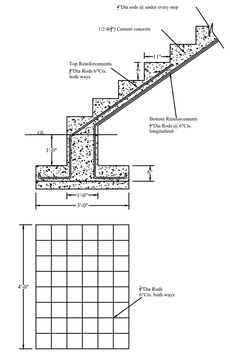

TYPICAL SECTIONAL DETAIL OF STAIR CASE

SCALE - 0-1" =2'-0"

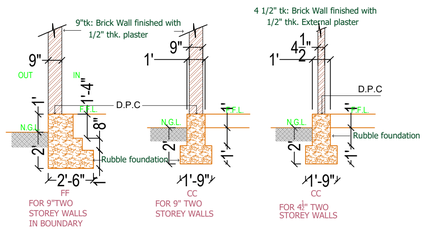

FOUNDATION DETAIL

SCALE : FOUR FEET TO AN INCH

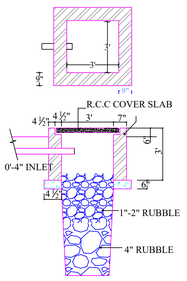

DETAIL OF SOAK PIT

SCALE - 0-1" =4'-0"

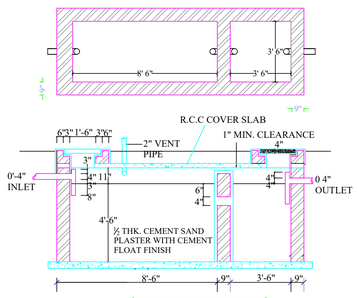

DETAIL OF SEPTIC TANK

SCALE - 0-1" =4'-0"

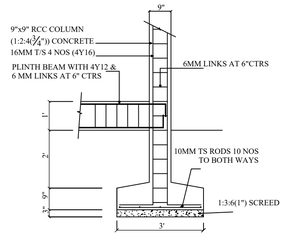

FOOTING SECTION (Z-Z)

SCALE- 2 FEET TO AN INCH

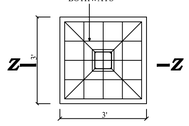

FOOTING DETAIL

SCALE- 2 FEET TO AN INCH

PROPOSED RESIDENCE FOR MRS.T.D.N.DE SILVA @ SOMAPALA MAWATHA, ISURUPURA,ANURADHAPURA.

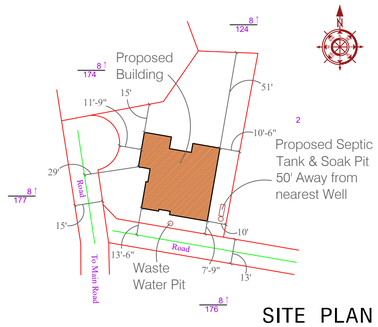

SITE PLAN

SCALE - 1:500

SCHEDULE OF DOORS & WINDOWS

TYPE	SIZE	DESCRIPTION	G.F.	F.F	TOTAL
D	4'-0"x8'-0"	DOUBLE SLASH TIMBER MAIN DOOR	01	01	02
D1	3'-0"x7'-0"	SINGLE SLASH TIMBER DOOR	03	02	05
D2	2'-6"x7'-0"	SINGLE SLASH TIMBER DOOR	01	01	02
DW	8'-0"x8'-0"	TIMBER SLIDING DOOR WINDOW	02	-	02
DW1	4'-0"x8'-0"	TIMBER SLIDING DOOR WINDOW	-	02	02
W	8'-0"x8'-0"	TIMBER GLAZED WINDOW	01	01	02
W1	4'-0"x5'-0"	TIMBER GLAZED WINDOW	01	01	02
W2	2'-6"x8'-0"	TIMBER GLAZED WINDOW	02	-	02
W3	4'-0"x4'-0"	TIMBER GLAZED WINDOW	01	01	02
W4	8'-0"x5'-0"	TIMBER GLAZED WINDOW	-	02	02
W5	2'-6"x5'-0"	TIMBER GLAZED WINDOW	-	02	02
F	2'-6"x2'-6"	FAN LIGHT	01	01	02